


INS. SANITARIA

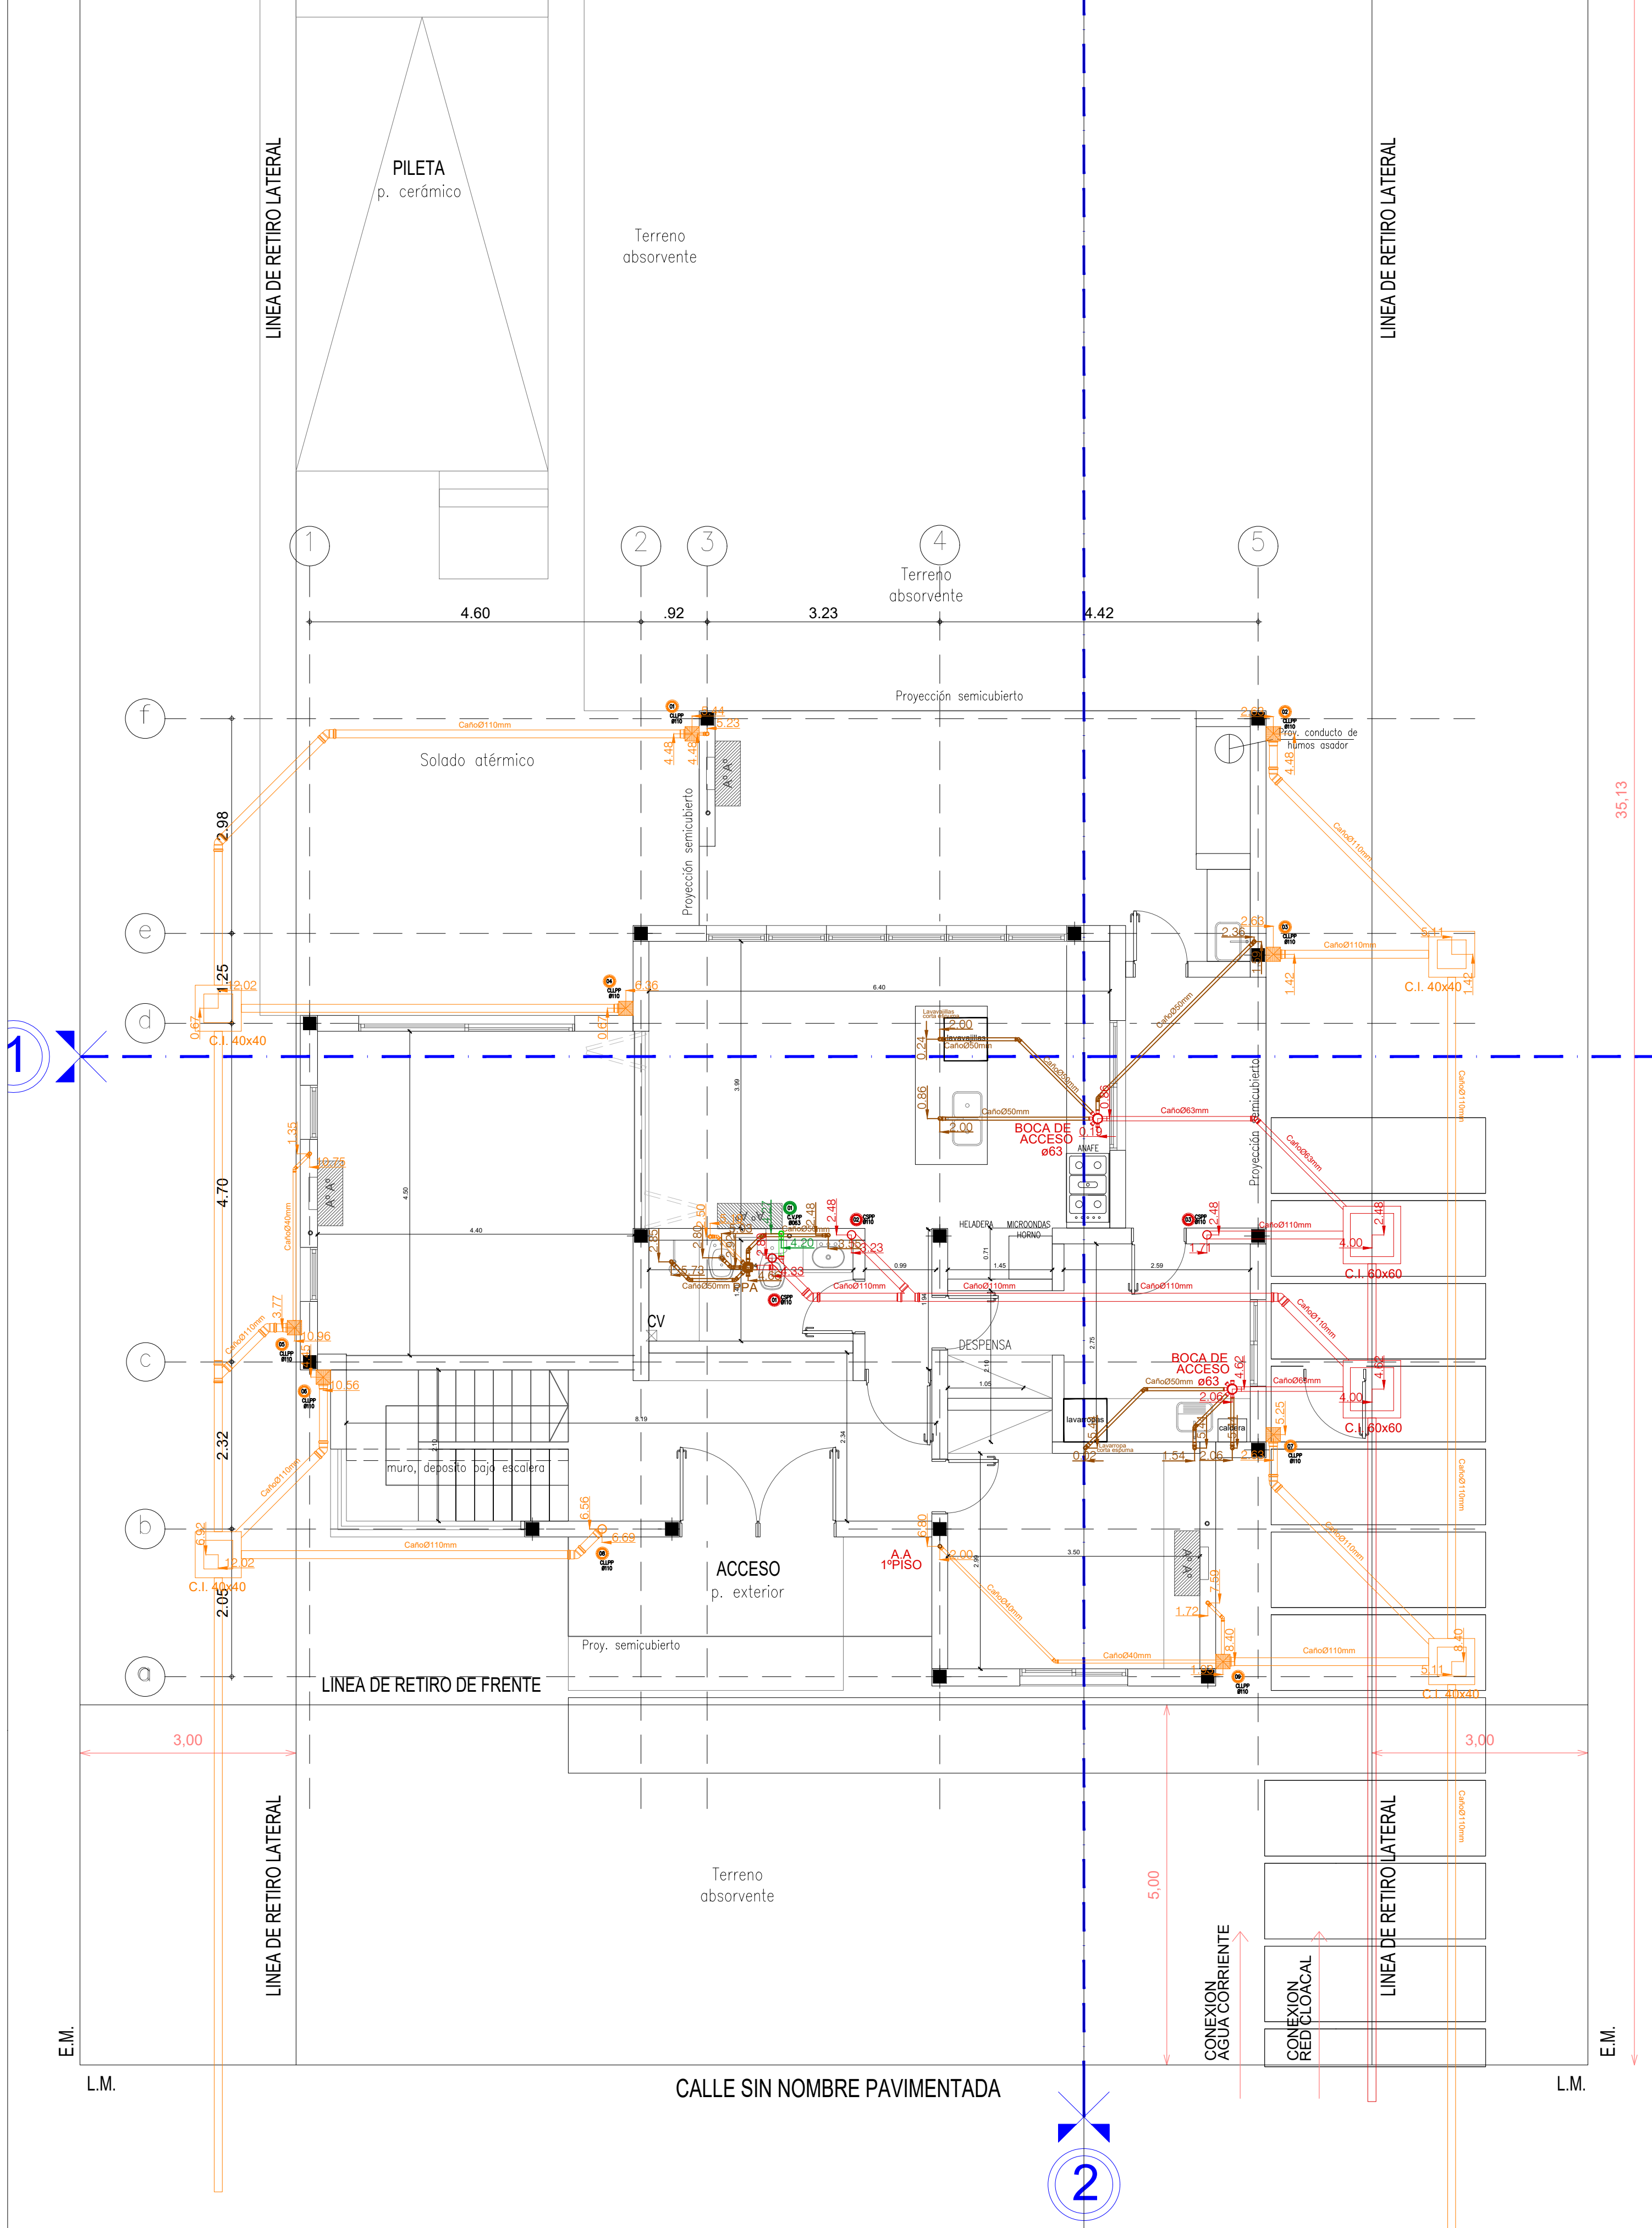

Profesional: ARQ. MATIAS IBAÑEZ
Cel: 1144025106
Mail: MATIAS@ARQ-INDUS.COM

Observaciones: las cotas acumuladas tienen como referencia su eje transversal

Plano:	INSTALACIONES PLANTA BAJA
--------	------------------------------

Fecha:	16/11/23	Escala:	1:50
--------	----------	---------	------

IS-01

Los Cardales
LOTE 413



OBSERVACIONES: ESTE PROYECTO ESTA PROTEGIDO POR EL ART.1 DE LA LEY 11.723. QUEDA PROHIBIDA SU REPRODUCCION Y/O CONSTRUCCION SIN LA DEBIDA AUTORIZACION